

A  
R  
C  
H  
I  
T  
E  
C  
T  
U  
R  
E



P  
O  
R  
T  
F  
O  
L  
I  
O

SAJAN KUSHWAHA

# RESUME

## EDUCATION

- 2022-PRESENT  
NEPAL ENGINEERING COLLEGE / BHAKTAPUR
- +2 / UNIGLOBE S.S COLLEGE / KAMALADI  
2076-2078
- PEACE POINT BOARDING SCHOOL / MID-BANESHWOR  
2075 PASSOUT / SCHOOL LEAVING CERTIFICATE

## EXPERIENCE

- ART TEACHER

## SOFTWARE

- AUTOCAD / SKETCHUP
- ADOBE PHOTOSHOP
- LUMION / D5 / ENSCAPE
- REVIT / BLENDER / DAVINCI RESOLVE
- MS OFFICE

## INTERESTS


- SKETCHING /PAINTING
- TRAVEL
- PHOTOGRAPHY

PHONE NUMBER  
9840024866

EMAIL:  
SAJAN43SINGH@GMAIL.COM

## ACADEMIC PROJECT


- RESIDENTIAL BUILDING
- SCHOOL (SECONDARY)
- COMMERCIAL BUILDING
- AGRICULTURE RESEARCH CENTER (POTATO)

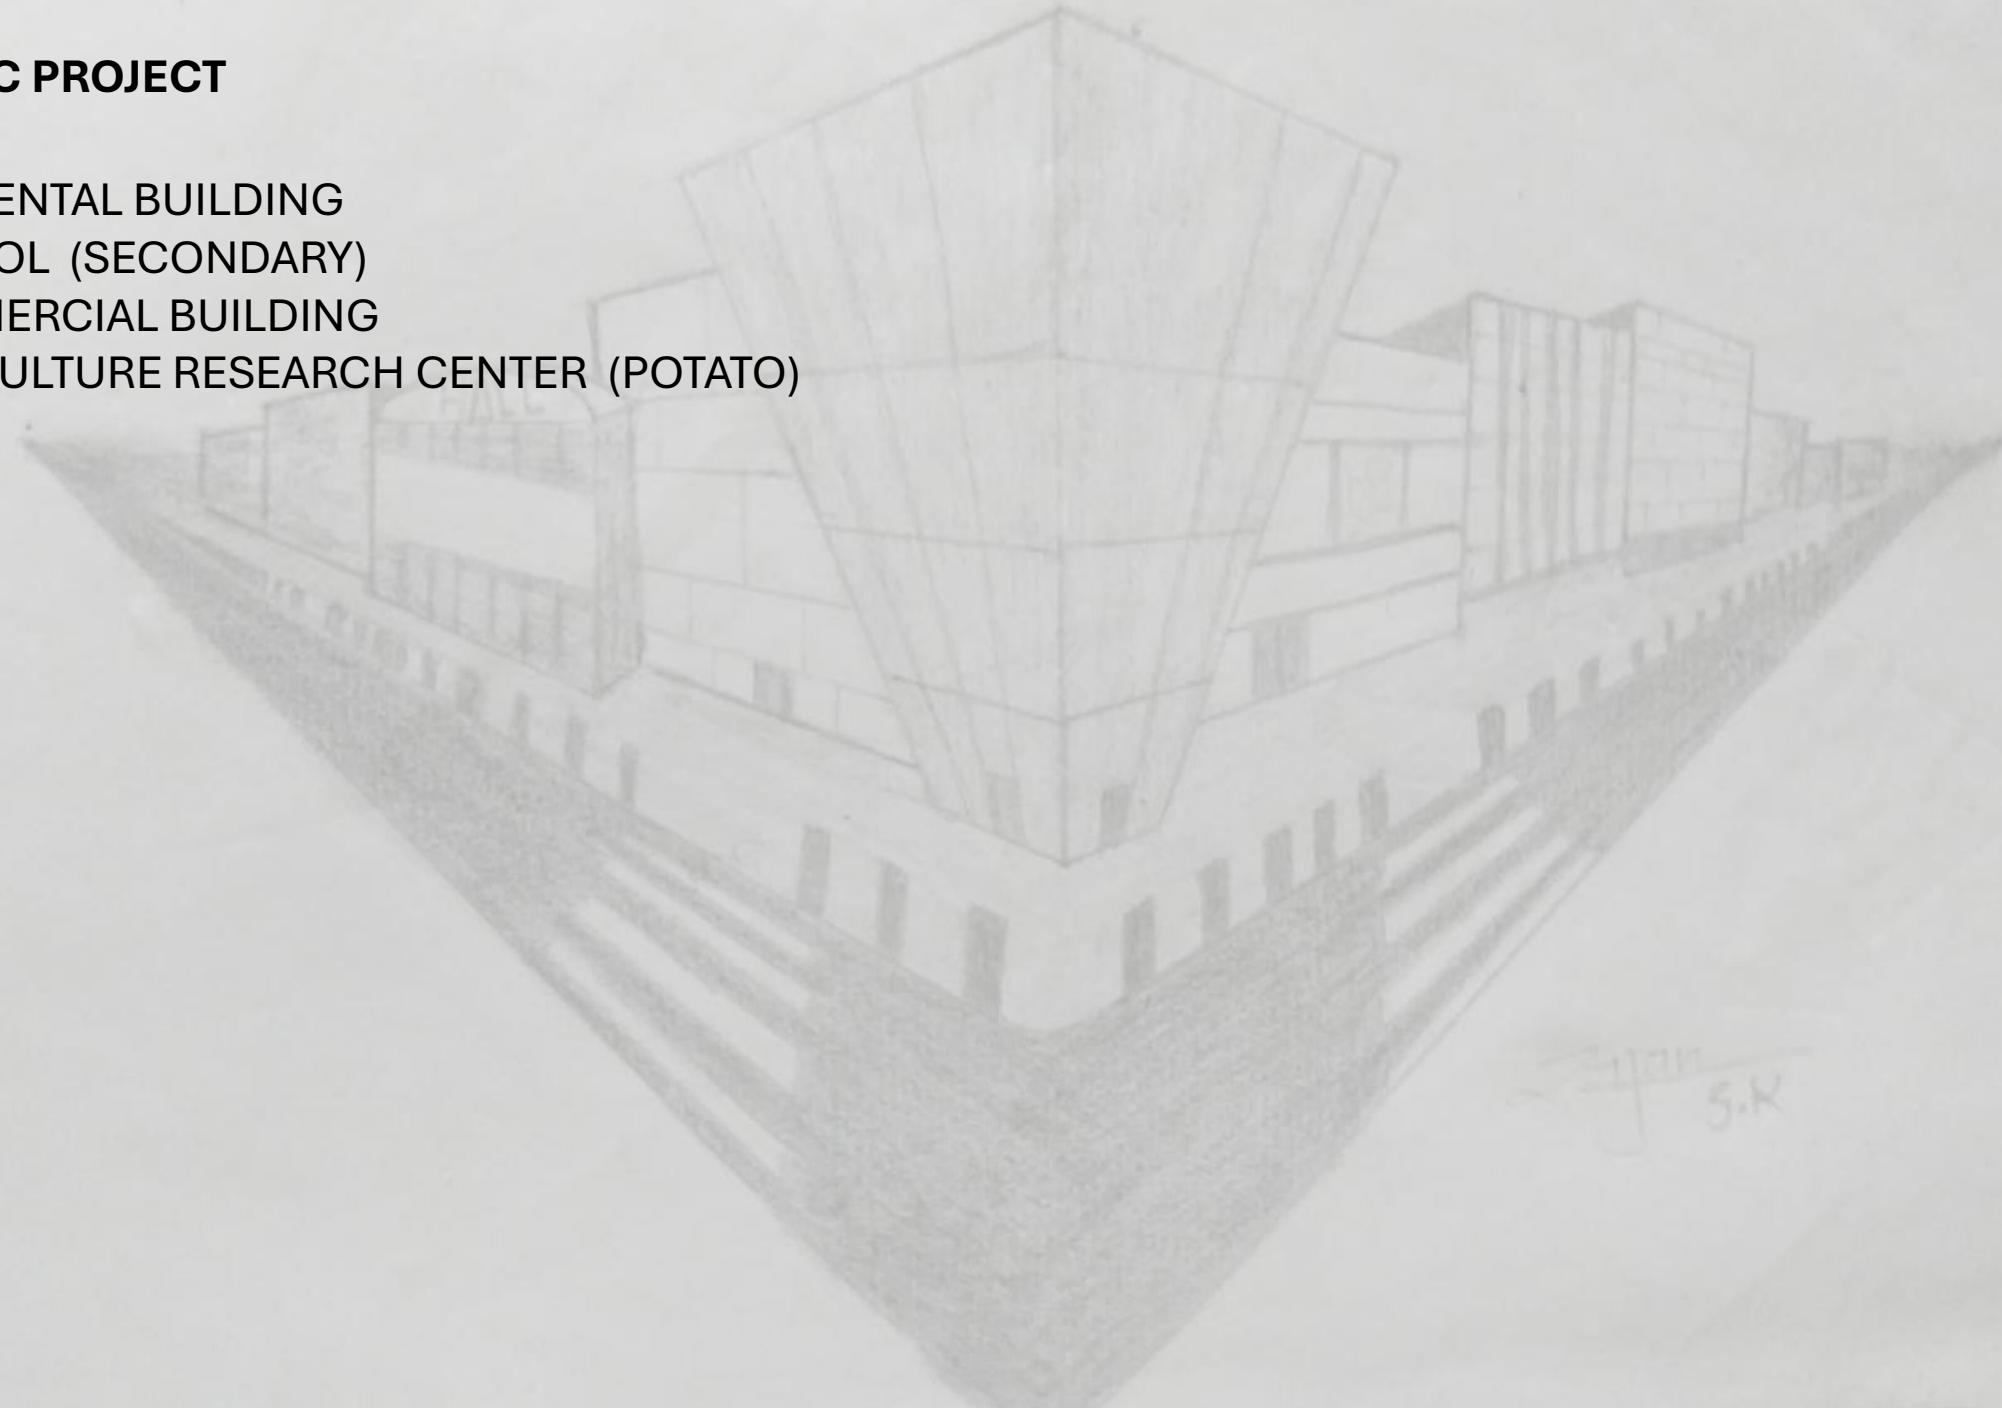


# MASTER PLAN





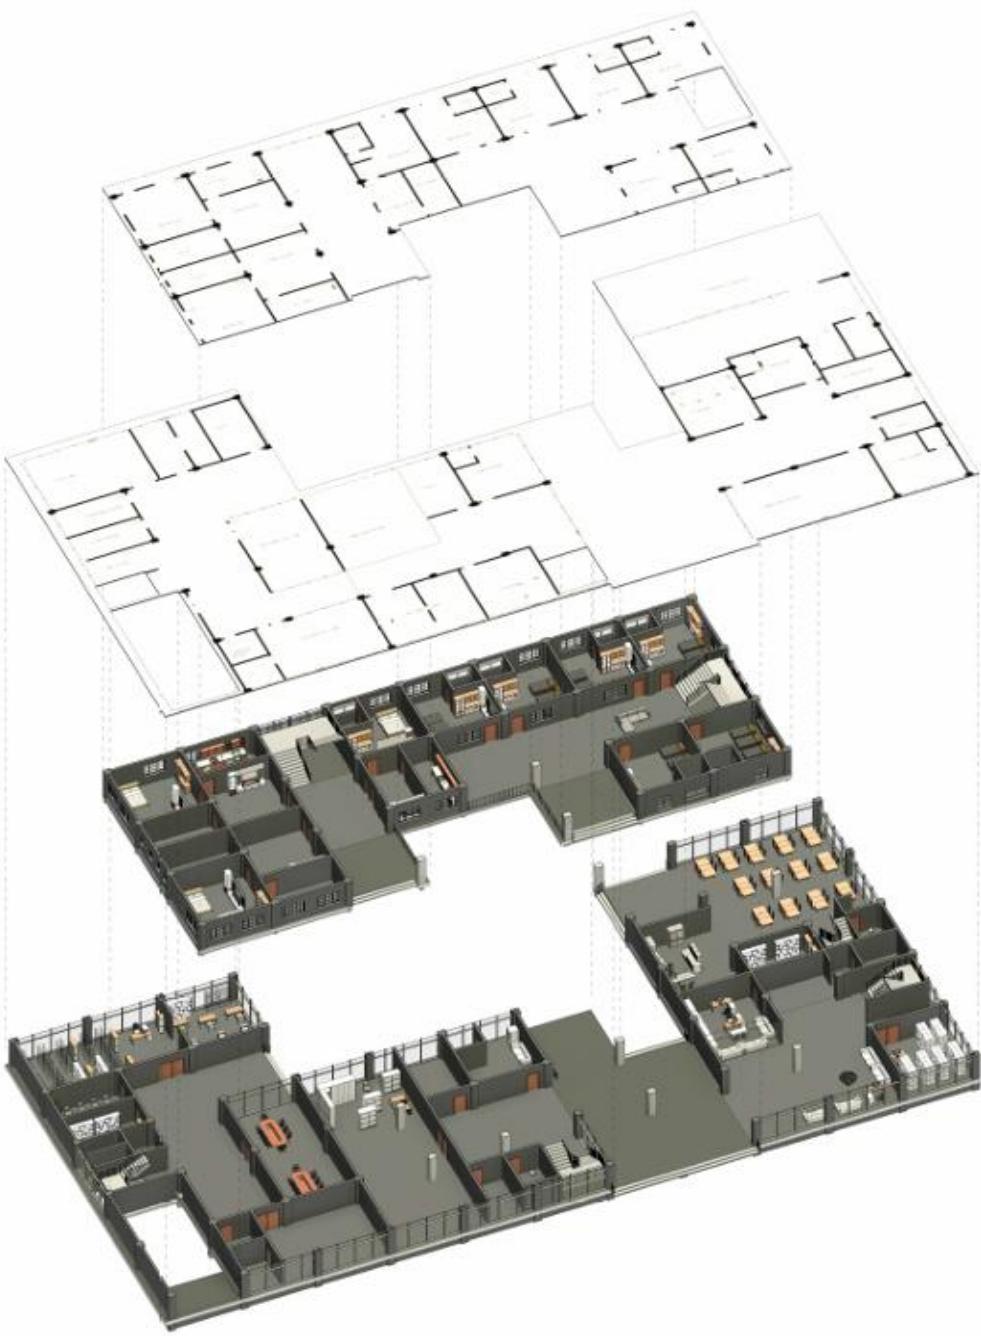

GROUND FLOOR PLAN WITH 2D AND 3D PLAN




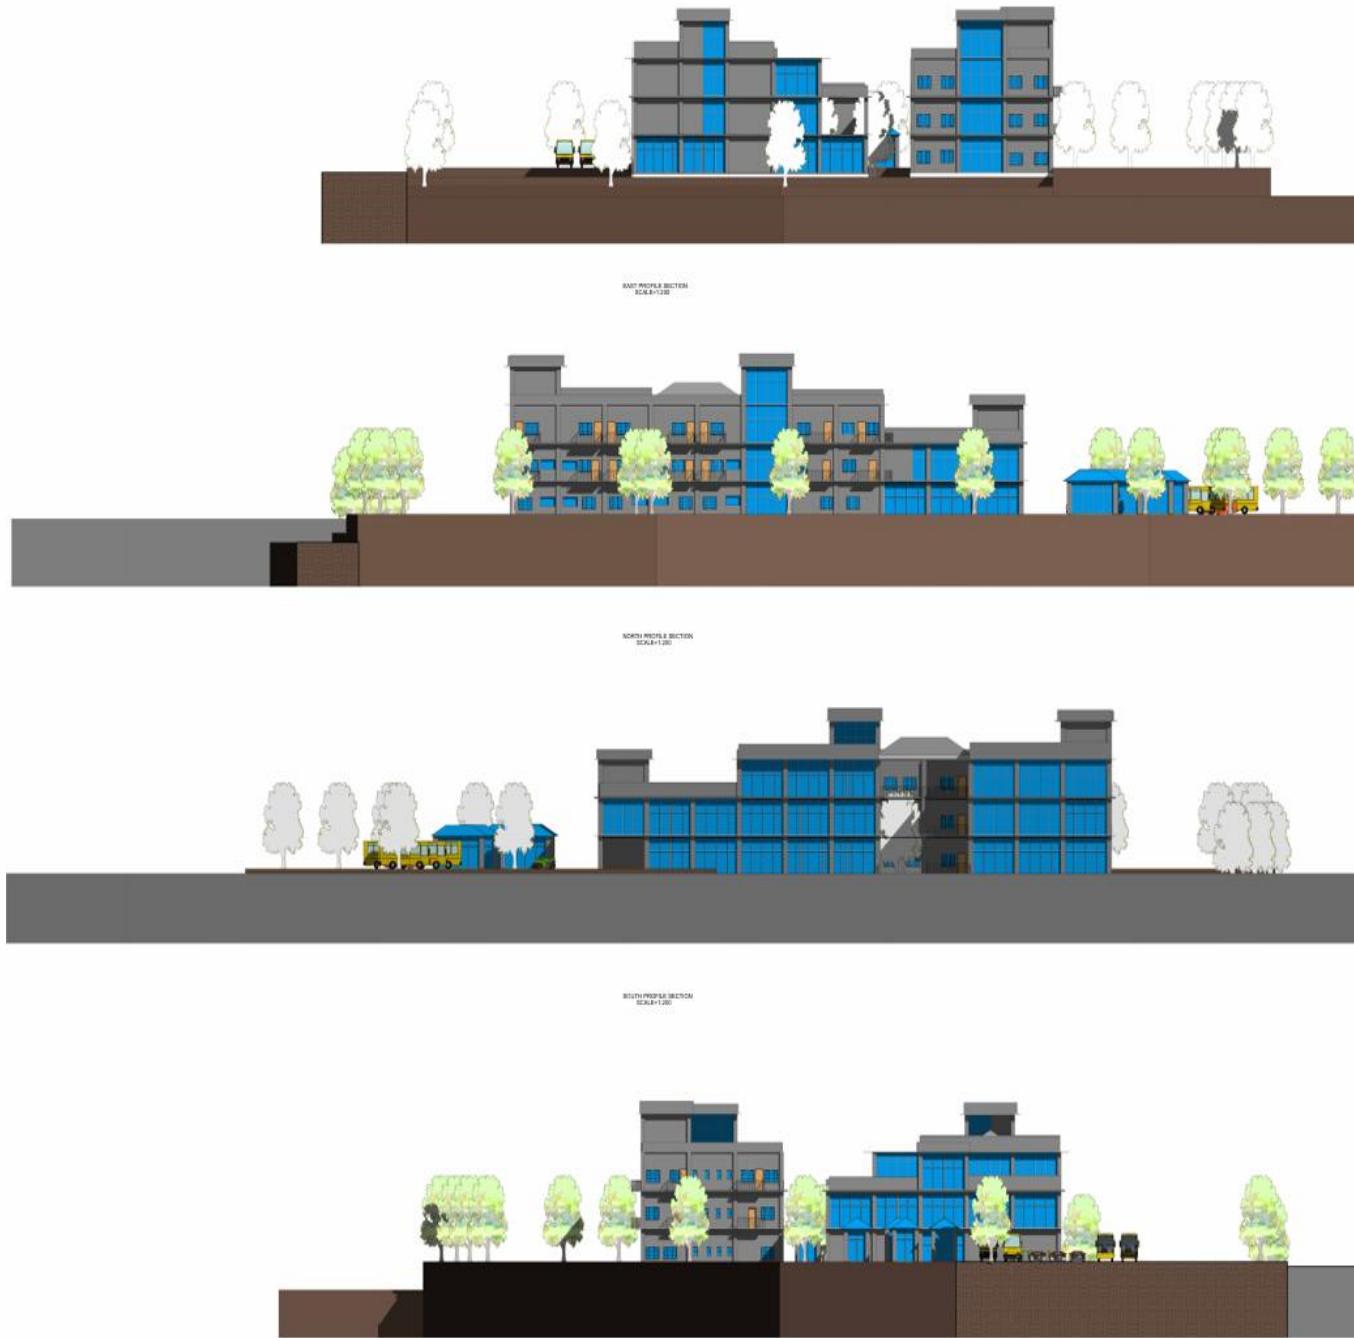





NORTH PROFILE SECTION  
SCALE=1:200



SOUTH PROFILE SECTION  
SCALE=1:200





EAST PROFILE SECTION  
SCALE=1:200


# HAND WORK

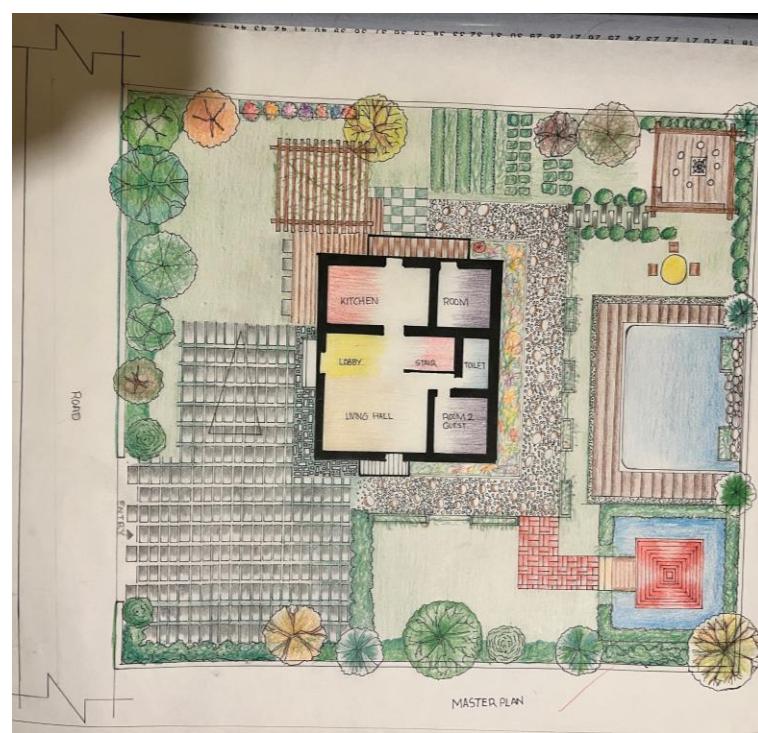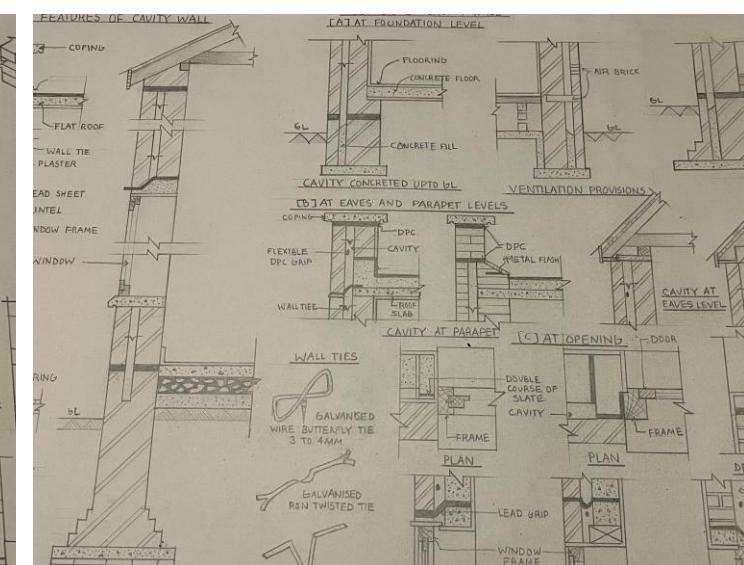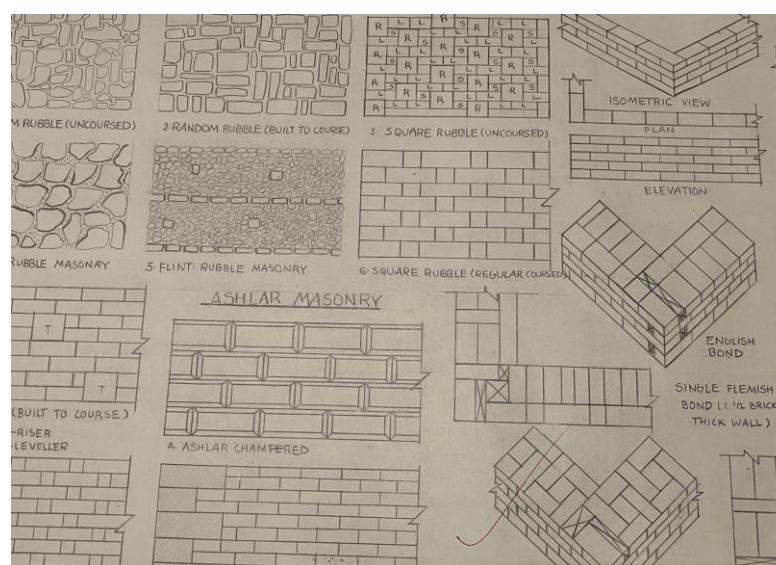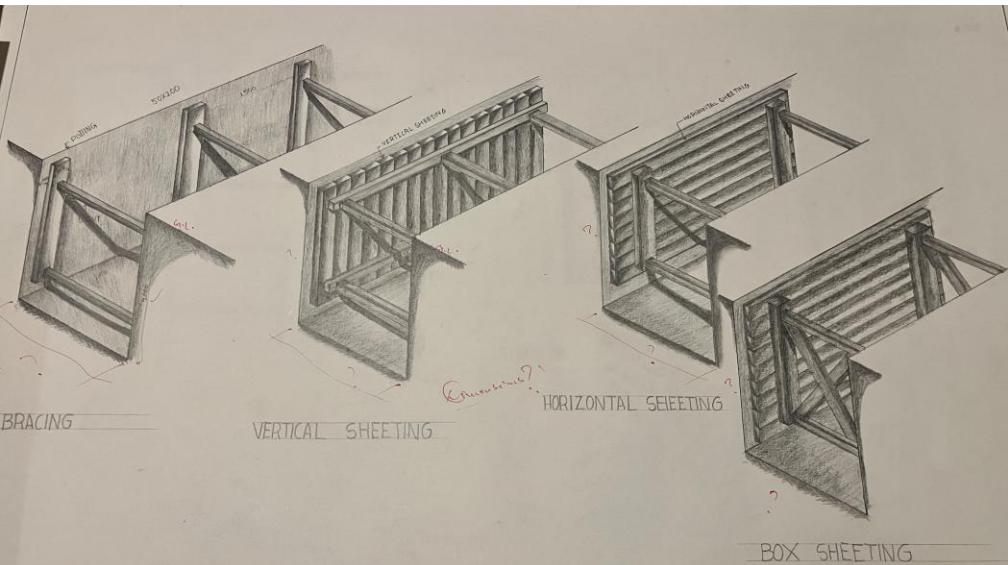

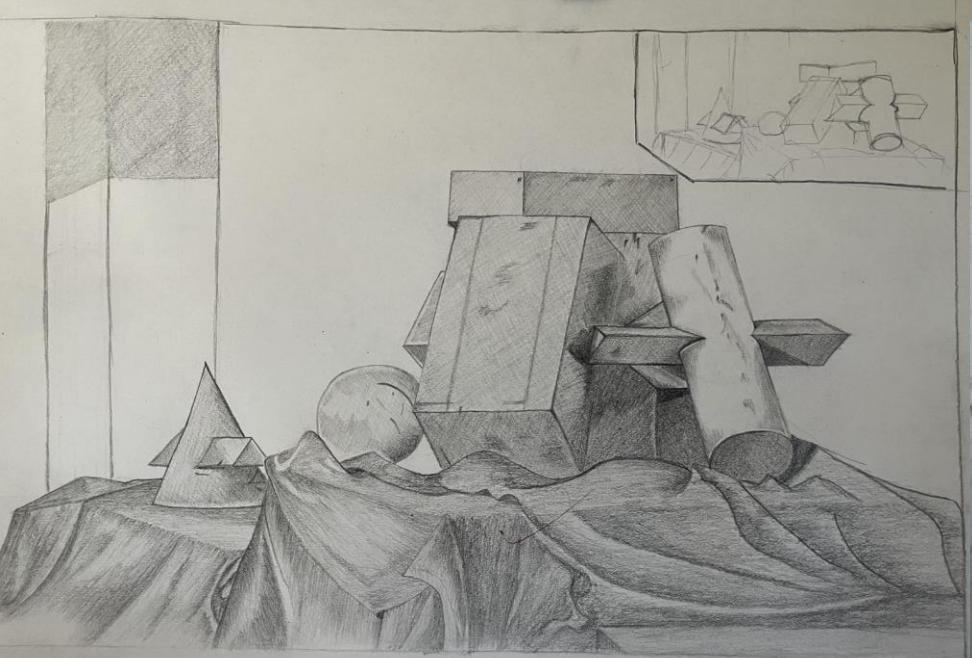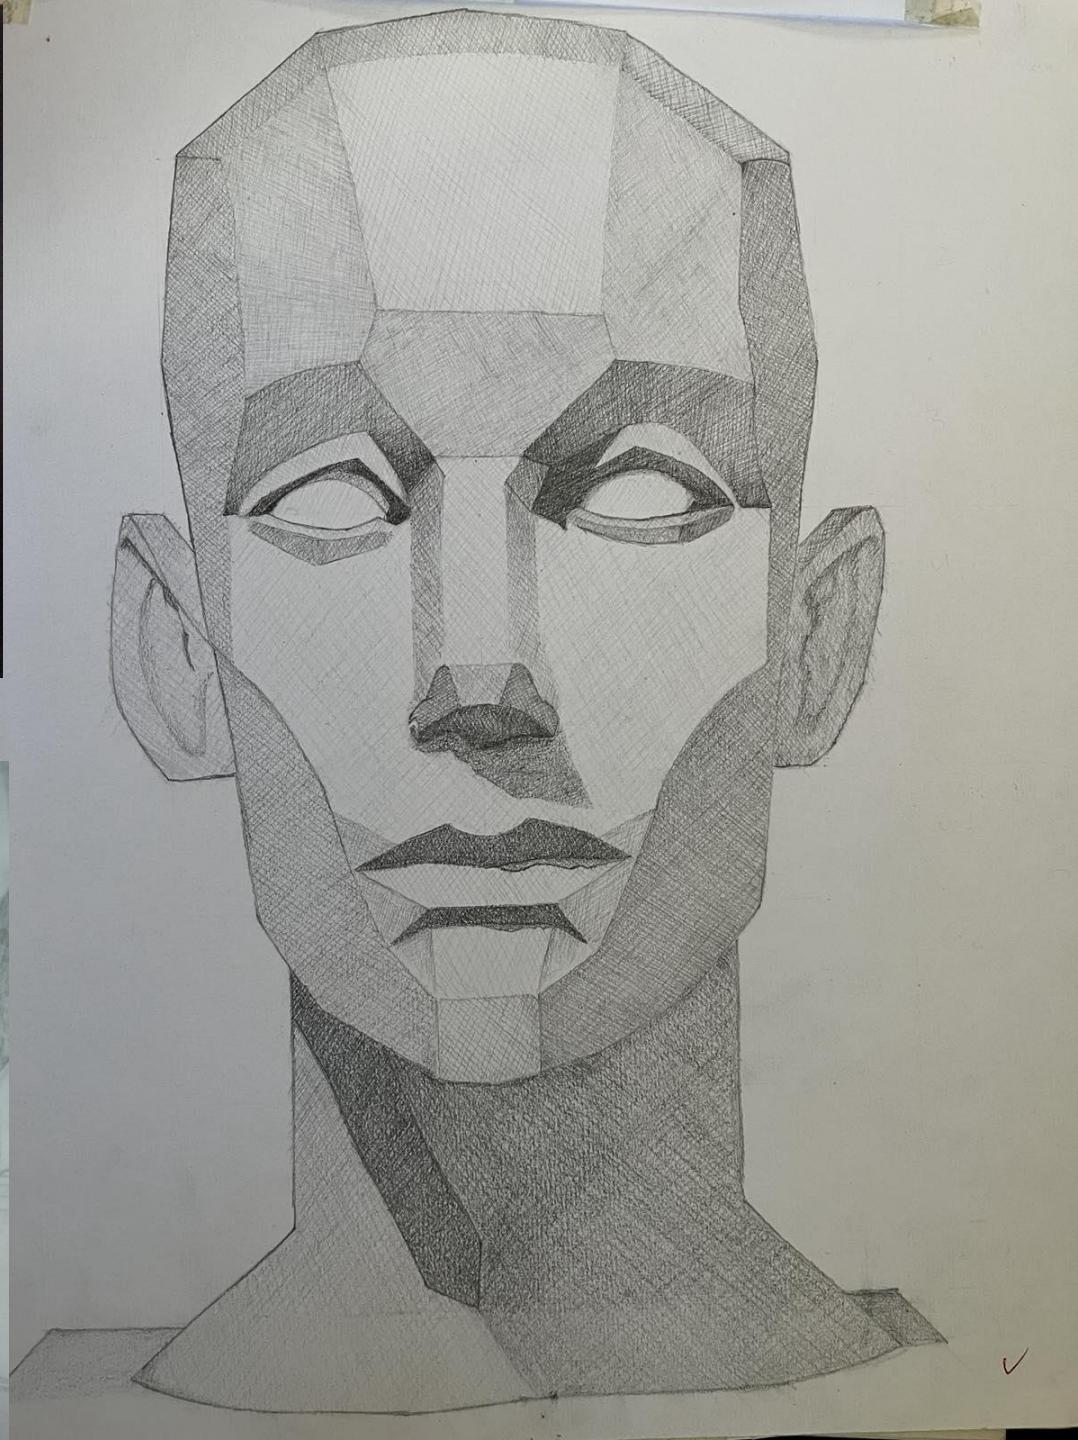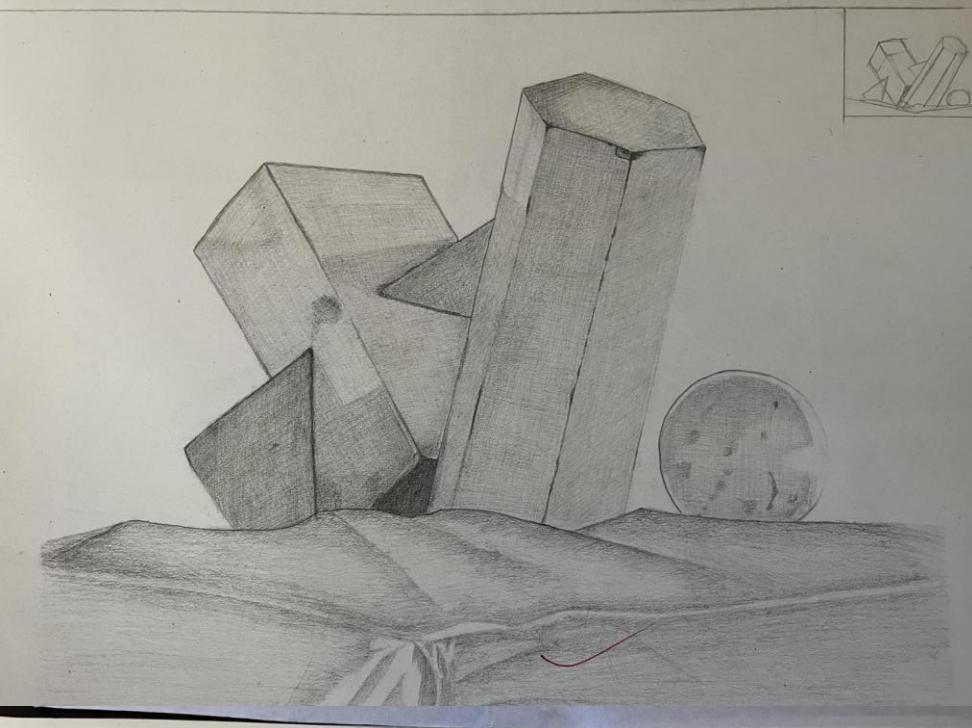

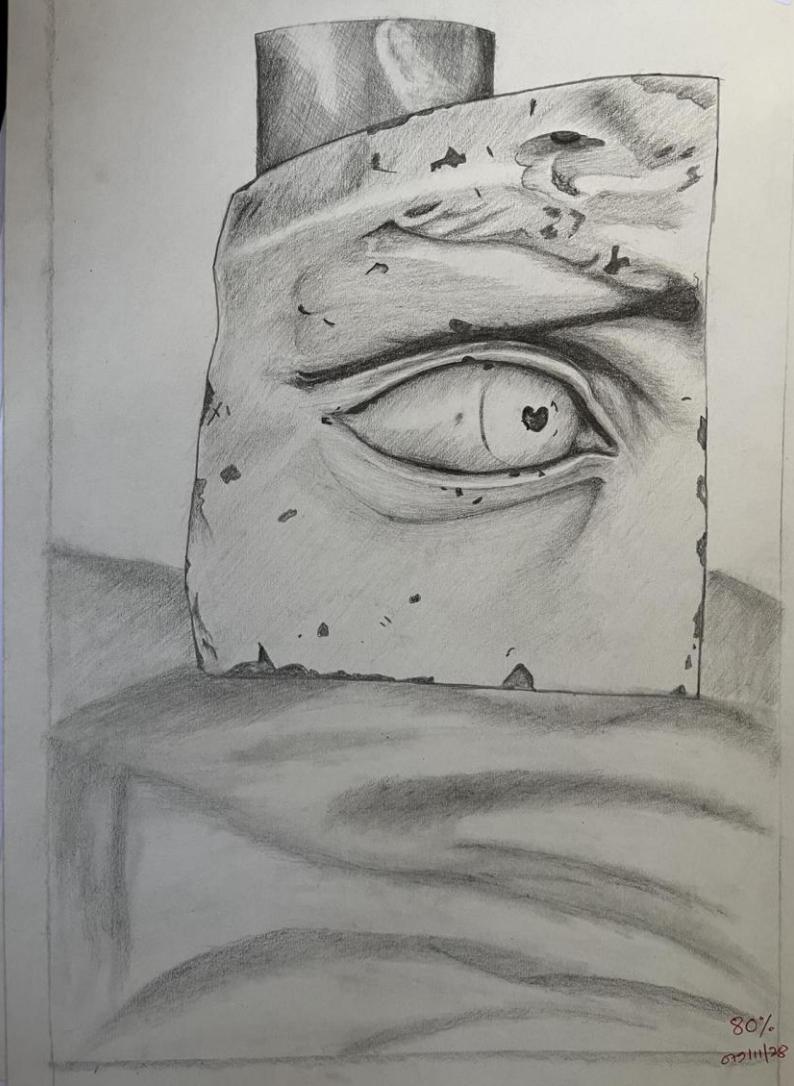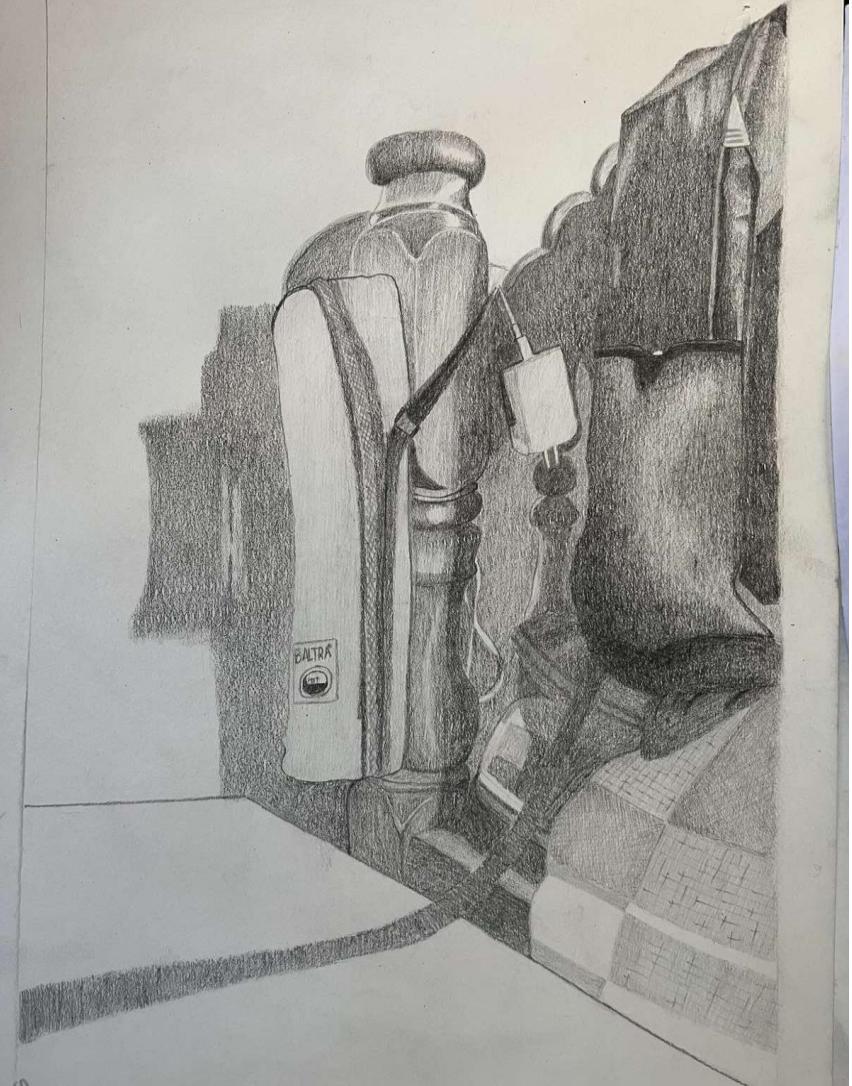

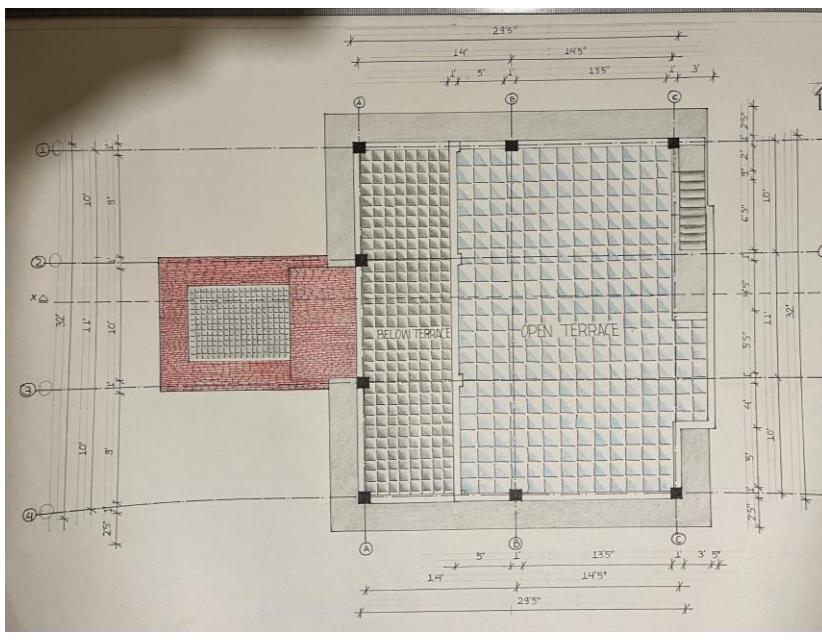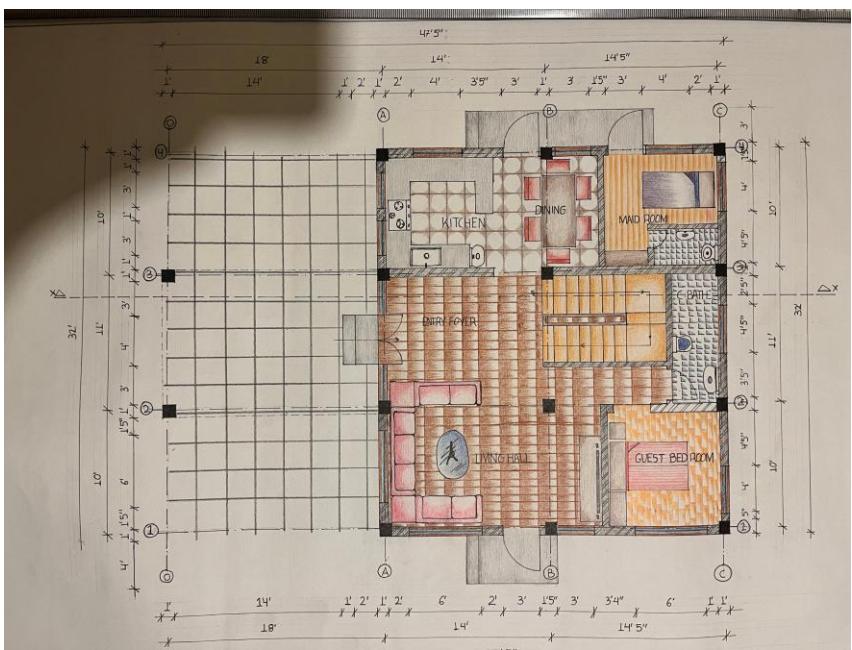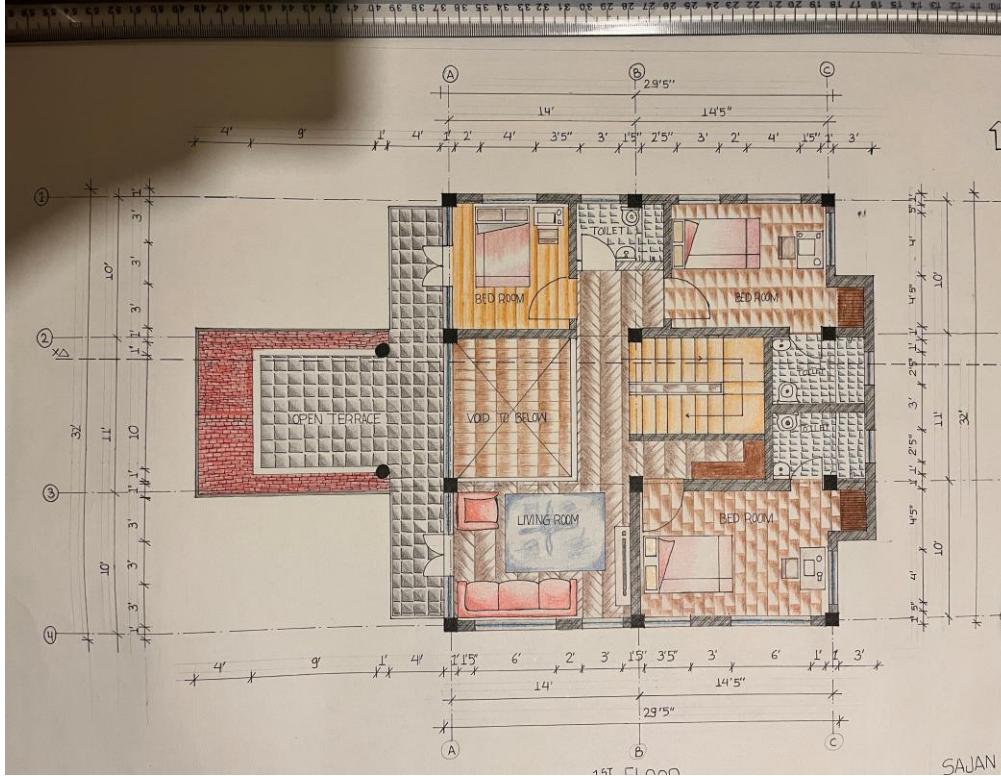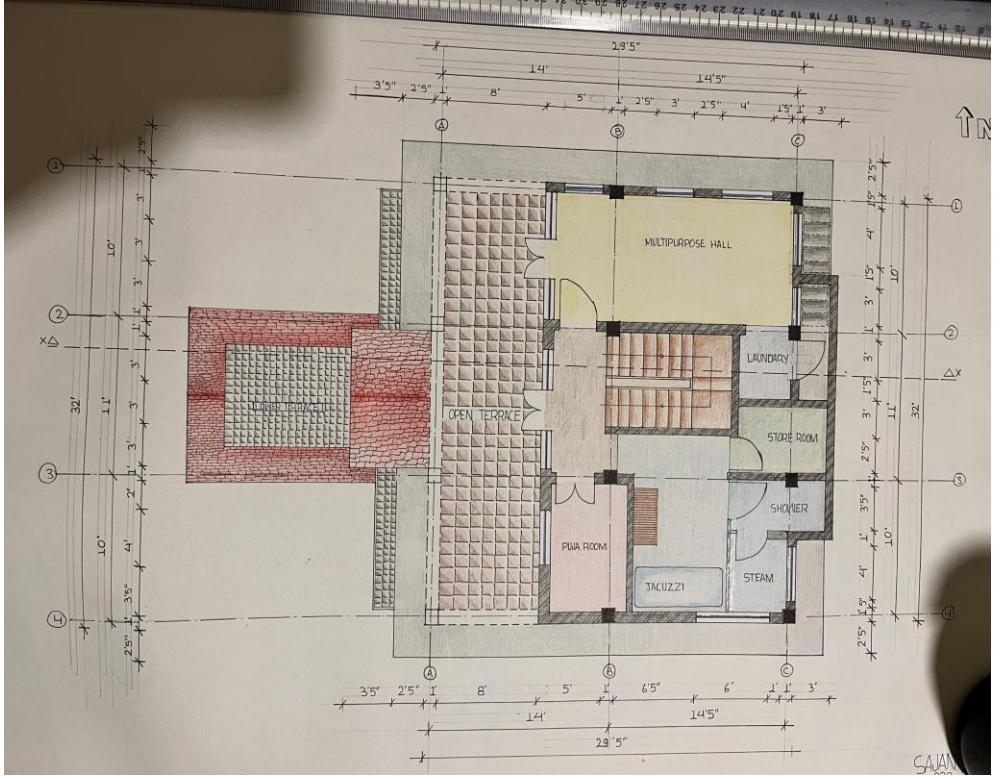

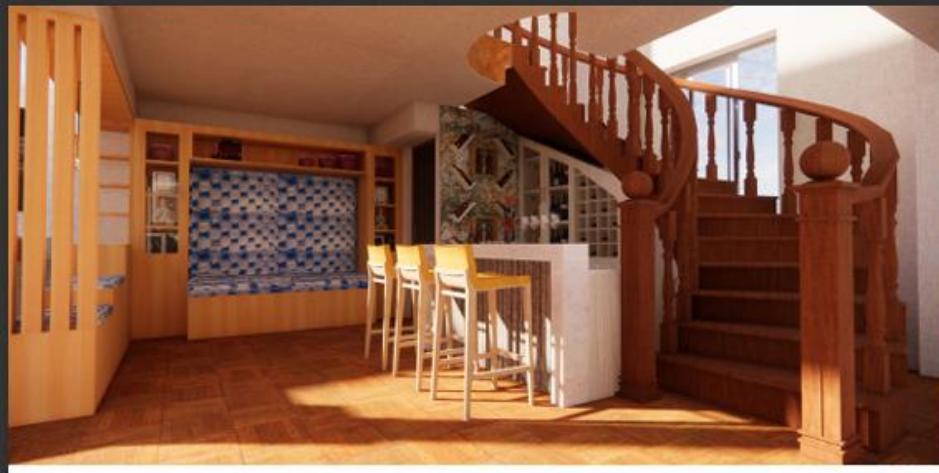

## SOME EXTRA WORKS OF FLOOR PLAN





DESIGNED FROM DIGITAL TOOLS/SOFTWARES



